
DECK 5 GENERAL ARRANGEMENT, MVZ 3, FR 100 TO FR 160

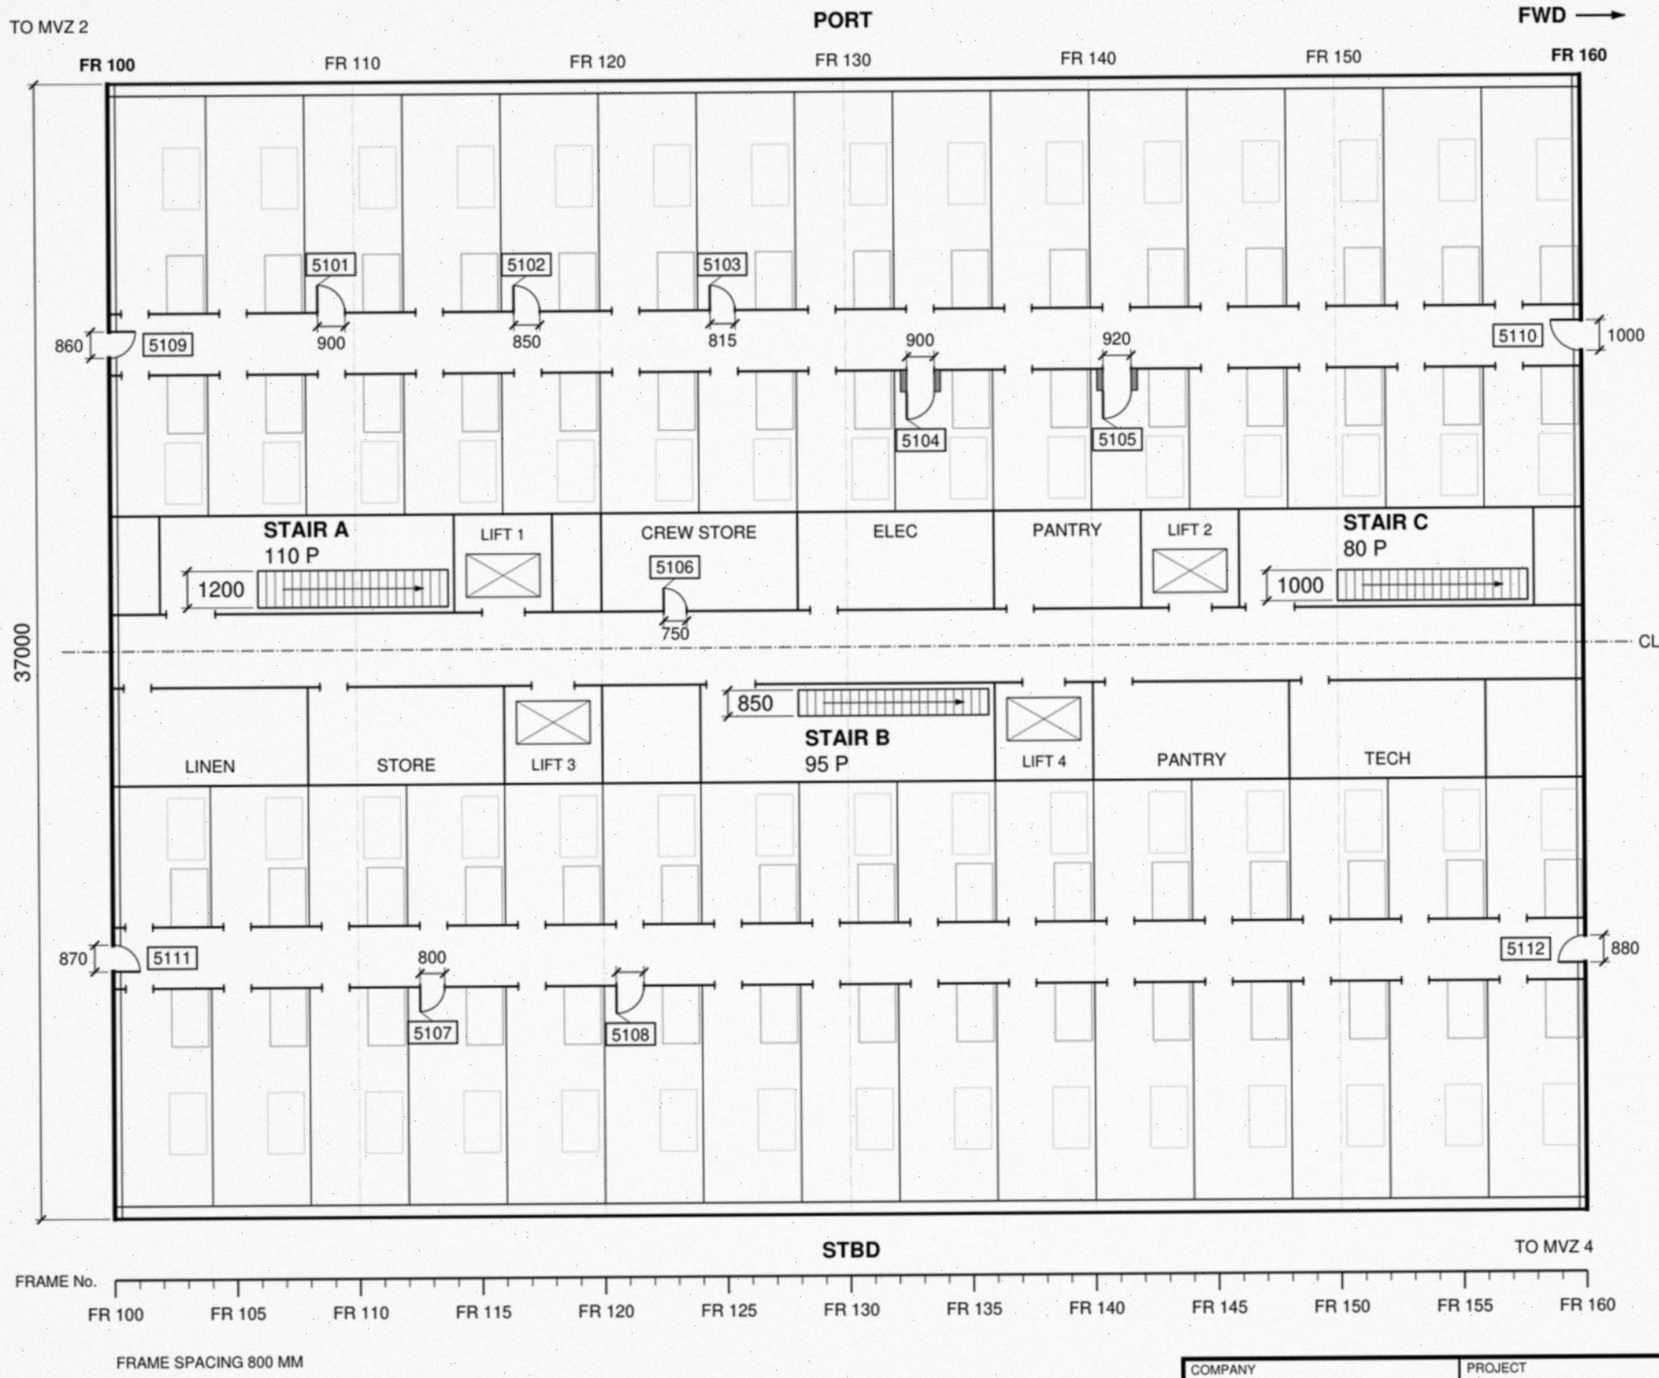

FRAME SPACING 800 MM

NOTES

1. DIMENSIONS IN MM.
2. DOOR AND STAIR WIDTHS SHOWN ARE CLEAR WIDTHS UNLESS NOTED.
3. P = PERSONS SERVED BY THE STAIR (ESCAPE ANALYSIS).
4. NUMBERED DOORS ARE LISTED IN DOOR SCHEDULE SYN-DS-105.
5. TYPICAL CABIN DOORS ARE NOT NUMBERED, SEE CABIN ARRANGEMENT DRAWINGS.
6. SYNTHETIC TEST DATA: not a real ship.


PARTICULARS OF SHIP (REFERENCE)

SYN-1 (synthetic cruise ship) HULL S-701
LOA 300.10 m
LPP 271.00 m
BREADTH MLD 37.00 m
FRAME SPACING 800 mm

LEGEND

- DOOR SWING, TAG = DOOR NUMBER
- STAIR: CLEAR WIDTH (MM), PERSONS SERVED (P)
- MVZ BOUNDARY (A-60 DIVISION)
- CORRIDOR AND CORE WALLS
- CABIN PARTITION
- FRAME LINE

KEY PLAN, NOT TO SCALE

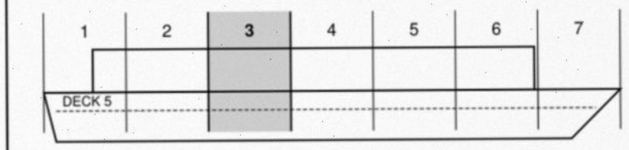

MAIN VERTICAL ZONES 1-7, THIS SHEET = MVZ 3

GRAPHICAL SCALE

0 5 10 15 m

REFERENCE DOCUMENTS

SYN-SPEC-001 OUTLINE SPECIFICATION, REV 2
SYN-DS-105 DOOR SCHEDULE DECK 5
EA-101 EVACUATION ANALYSIS, REV 1
SYN-GA-104 AND SYN-GA-106 GA DECKS 4 AND 6

REV	DATE	DESCRIPTION	BY	CHKD
A	2026-10-01	FIRST ISSUE	GEN	GEN

COMPANY: SYNTHETIC YARD (INVENTED)	PROJECT: SYN-1 (synthetic cruise ship) YARD HULL S-701			
TITLE: **GENERAL ARRANGEMENT DECK 5 (MVZ 3)**				
DRAWING NO.: SYN-GA-105	REV: A	DATE: 2026-10-01	SHEET SIZE A3	SCALE 1:100
DRAWN: SYN-GEN (SCRIPT)	CHECKED: N/A (SYNTHETIC)	SHEET: 1 OF 1	SYNTHETIC TEST DATA: not a real ship	